

LOT 2, BLOCK 14, FIRST REPLAT IN PORT ST LUCIE INDUSTRIAL PARK UNIT ONE,
ACCORDING TO THE PLAT THEREOF, AS RECORDED IN PLAT BOOK 23, AT PAGES 6, 6A
THROUGH 6D, OF THE PUBLIC RECORDS OF ST. LUCIE COUNTY, FLORIDA.

PCN				3435-601-0006-000-2
ZONING				GENERAL COMMERCIAL
FUTURE LAND USE				COMMERCIAL GENERAL
EXISTING USE				CARWASH
PROPOSED USE				CARWASH
MIN. BUILDING SETBACKS				FRONT 25', SIDES 10', REAR 10'
PROVIDED SETBACKS				FRONT 54', SIDES 29' & 42', REAR "2.89"
				*VARIANCE P 19-242
		SF	AC	%
TOTAL SITE AREA		46,728	1.073	100.0%
IMPERVIOUS AREA		33,121	0.76	70.9%
EXISTING BUILDINGS		5,421	0.12	11.6%
PROPOSED CANOPIES		1,500	0.03	3.2%
EXISTING PARKING / VUA		25,038	0.57	53.6%
EXISTING CONCRETE WALKS, RAMPS, ETC...		1,162	0.03	2.5%
PERVIOUS AREA		13,607	0.31	29.1%
LANDSCAPE AREA		13,607	0.31	29.1%
PARKING		REQ.	PROVIDED	
TOTAL SPACES (1/ 200 SF OF FLOOR SPACE 1,360/200)		7	10	
ADA ACCESSIBLE SPACES		1	1	

1. All signs shall meet City of Port Saint Lucie Land Development Regulations.
2. All exotic vegetation to be removed prior to the issuance of a Certificate of Occupancy.
3. There is to be an irrigation system installed to ensure continued growth of all planting areas.
Source of irrigation water to be potable water.
4. Any proposed lighting will be directed away from any residential units or adjacent roadways.
5. No upland preserves exist on the site.
6. The site has been cleared and built.
7. Water and Sewer provided by PSLUSD
8. The property owner, contractor, and authorized representatives shall provide pickup, removal, and disposal of litter within the project limits and shall be responsible for maintenance of the area from the edge of pavement to the property line within the City's right-of-way in accordance with City Code, Section 41.08 (g)

The existing 1.07-acre ± site located along US1, and Huffman Road is currently being operated as a car wash. The project is served by site grading that directs stormwater to drainage inlets and perimeter swales that convey to the central dry detention swale with an exfiltration trench providing all required water quality pretreatment and attenuation prior to discharge into the adjacent Huffman Road public right-of-way. The existing stormwater management system provides all water quality and attenuation in accordance with the City of Port St. Lucie and SFWMD criteria for this location.

The existing 1.07-acre ± site located along US1, and Huffman Road is currently being operated as a car wash. The site has operated as such for many decades without any issue circulating motor vehicles in an orderly fashion. The trip generation is as follows.

The ITE trip generation, 11th edition. Category: Self Service Car Wash (947) (per wash stall) (average rates utilized)	average rate	number of stalls	trips
Weekday daily trips:	108.00 / per stall	7	756
A.m. peak hour trips:	8.00 / per stall	7	56
P.m. peak hour trips:	8.00 / per stall	7	56

HANDICAP SPACE DETAIL


REGULAR SPACE DETAIL

NOTES:


1. TOP PORTION OF FTP 25 & 26 SHALL HAVE A REFLECTIVE BLUE BACKGROUND WITH WHITE REFLECTIVE SYMBOL AND BORDER.
2. BOTTOM PORTION SHALL HAVE A REFLECTIVE WHITE BACKGROUND WITH BLACK OPAQUE LEGEND AND BORDER
3. FTP 25 & 26 MAY BE FABRICATED ON ONE PANEL OR TWO.
4. FTP 25 IS FOR USE IN AREAS WHERE SPACE IS LIMITED

Diagram illustrating the proposed dumpster enclosure layout. The enclosure is a square structure with a width of 12' and a height of 7'. It features a 5' masonry wall on the left side, a dumpster on the right side, and a concrete slab with a thickened edge. The enclosure is supported by metal gates with opaque covering, which are hinged to the asphalt drive.

Land Planner: Michael T. McCarty McCarty & Associates Land Planning and Design LLC 309 SE Osceola Street Suite 104, Stuart, FL 34994 mike@mccartylandplanning.com 772-341-9322	Surveyor: Velcon Engineering & Surveying, LLC 1449 Commerce Center Drive Port St. Lucie, FL 34986 nfo@velconfl.com 772-879-0477	Owner: Antema Corporation 1313 Ponce De Leon Blvd # 200 Coral Gables, FL 33134-3343 juelle@gmail.com 787-464-2401
--	---	---

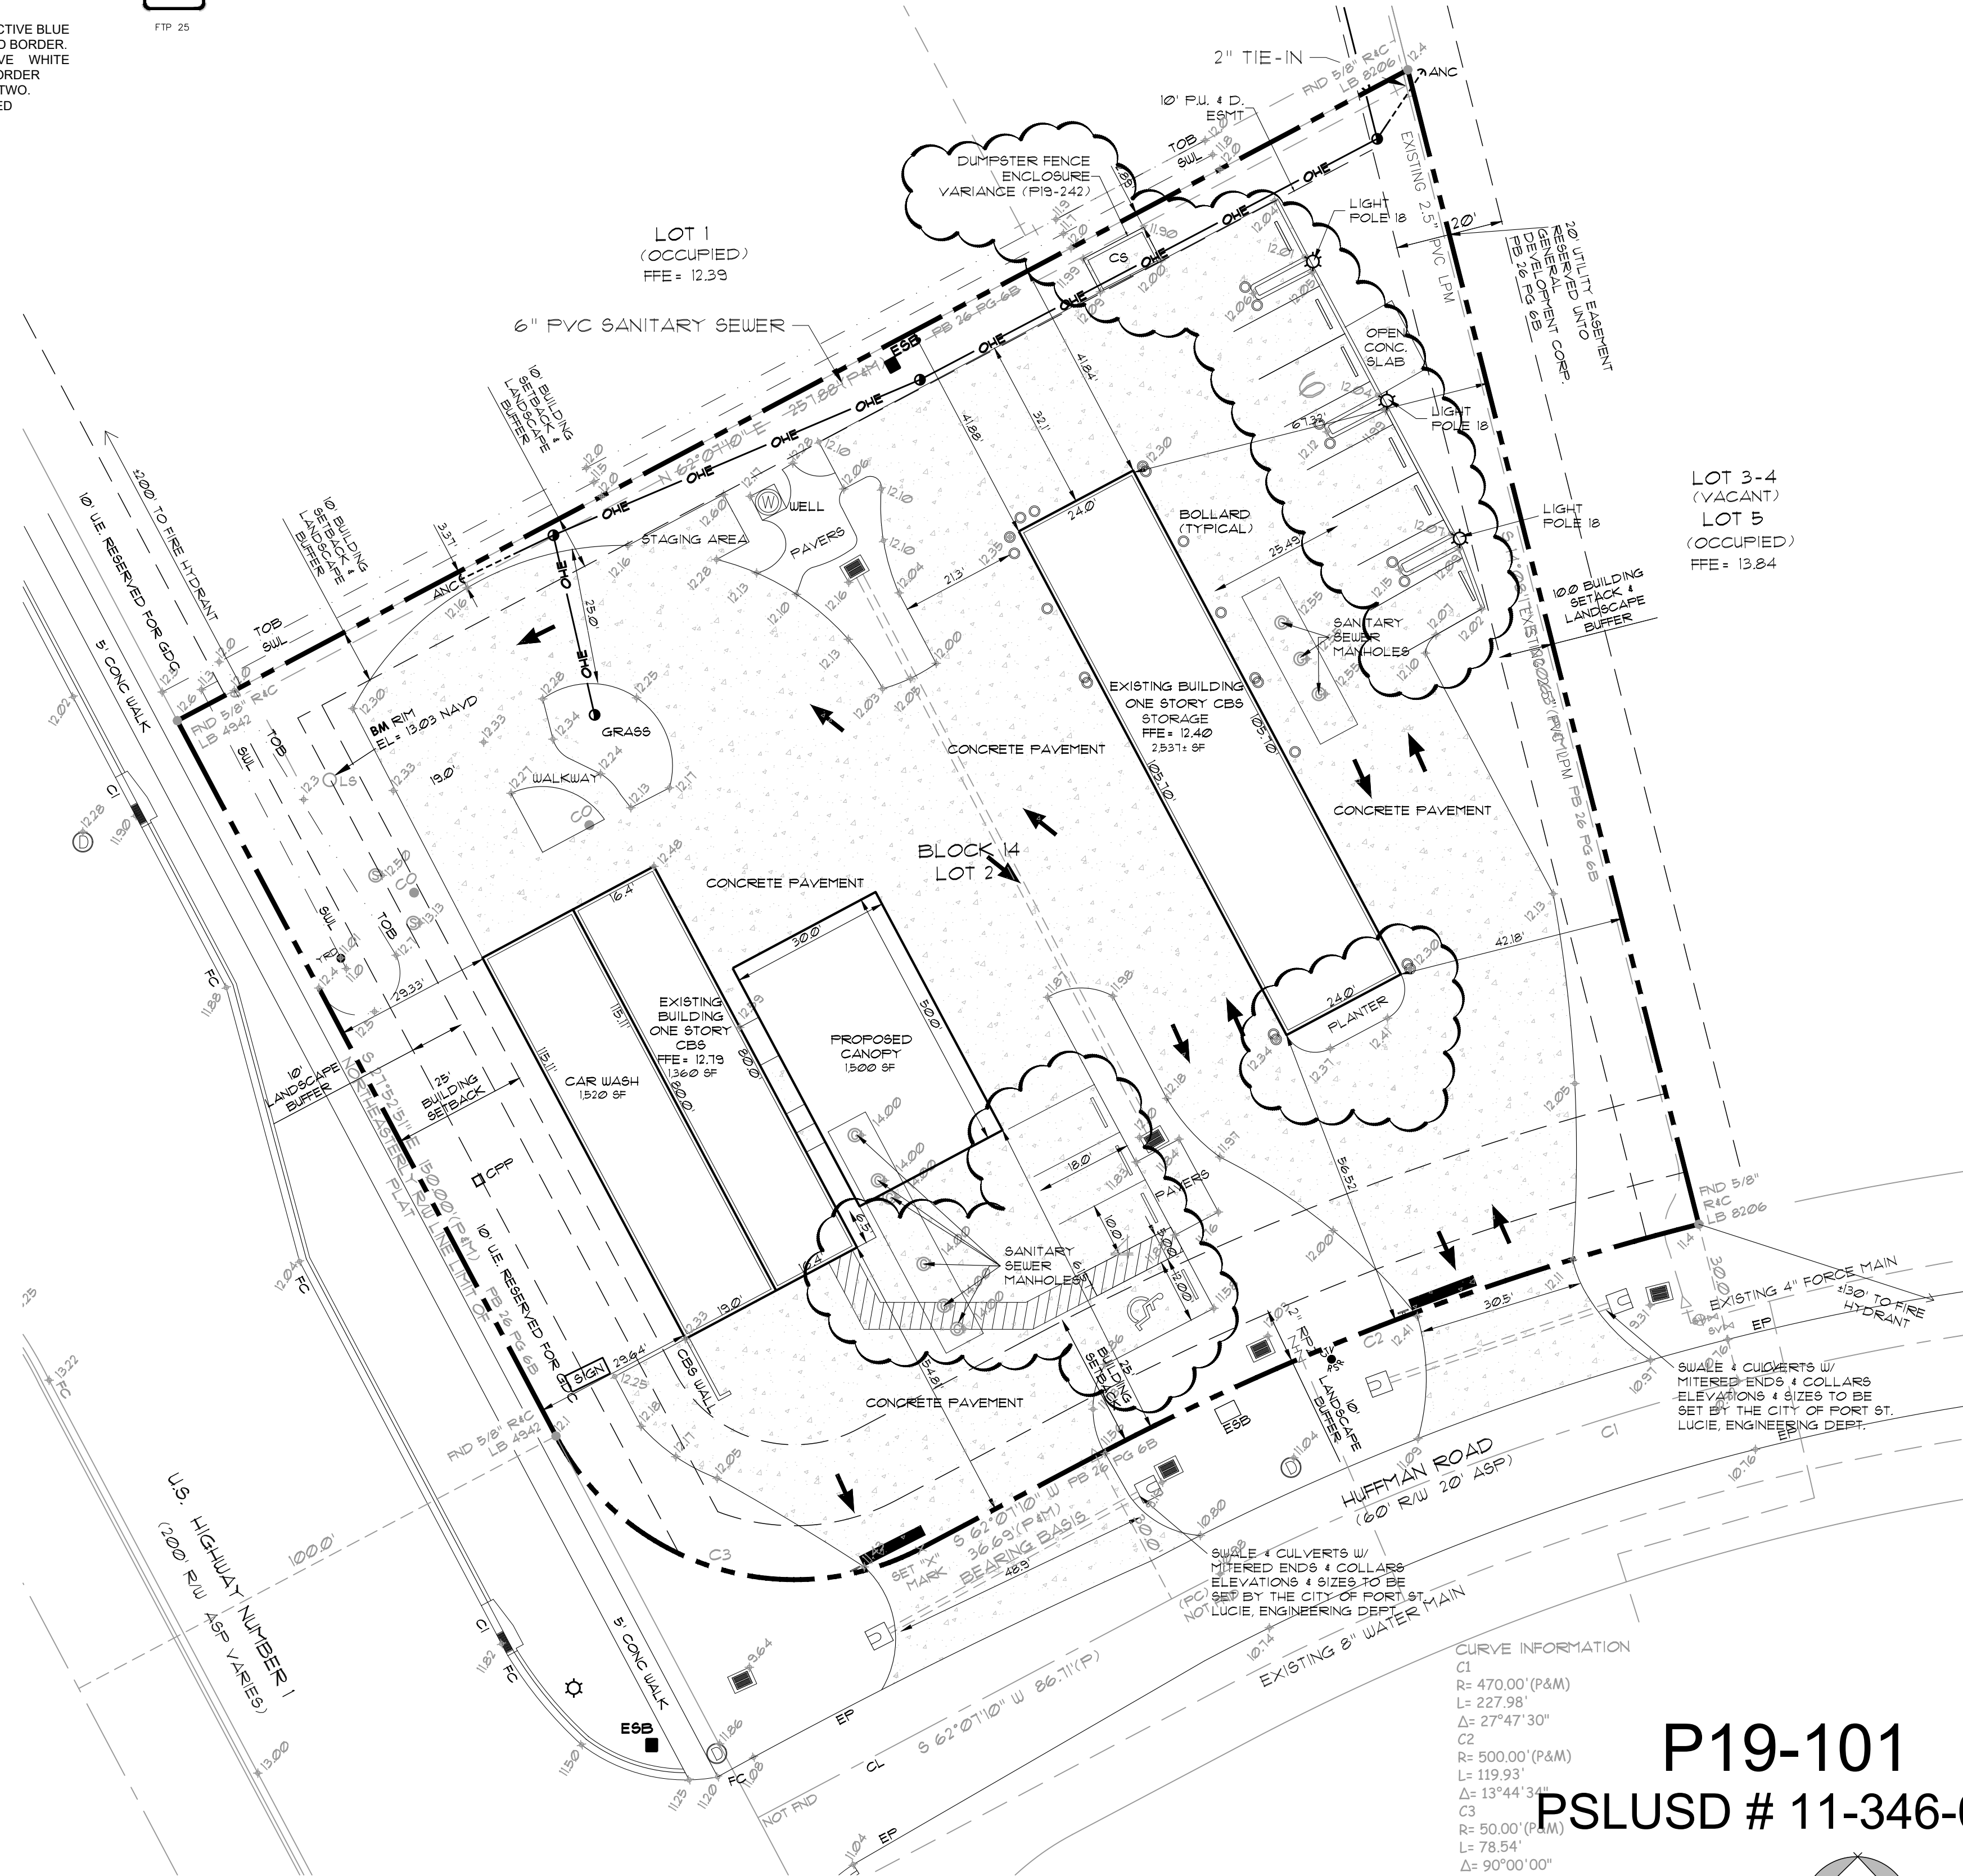

Age Group	Percentage
0'	10%
10'	10%
20'	10%
40'	70%

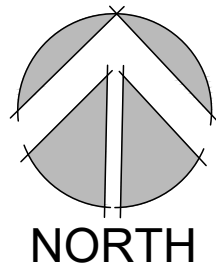

McCARTY & ASSOCIATES

LAND PLANNING
AND DESIGN

STUART • FT. PIERCE

772.341.9322
www.McCartyLandPlanning.com
Mike@McCartyLandPlanning.com

Highline Carwash

1401 Huffman Road
Port Saint Lucie, Florida

Site Plan Amendment



Drawn By	DMS
Checked By	MM
Scale	1" = 20'-0"
Drawing Date	1/16/20
	10/16/24
	1/14/25
	1/22/25
	3/25/25 4/3/25

S-1