FEDERAL AVIATION ADMINISTRATION
1A SURVEY

NOTE: COORDINATES BASED ON NAD (83/90) AND REFERENCED TO LOCAL NGS MONUMENTS BY DIFFERENTIAL GPS SURVEY.

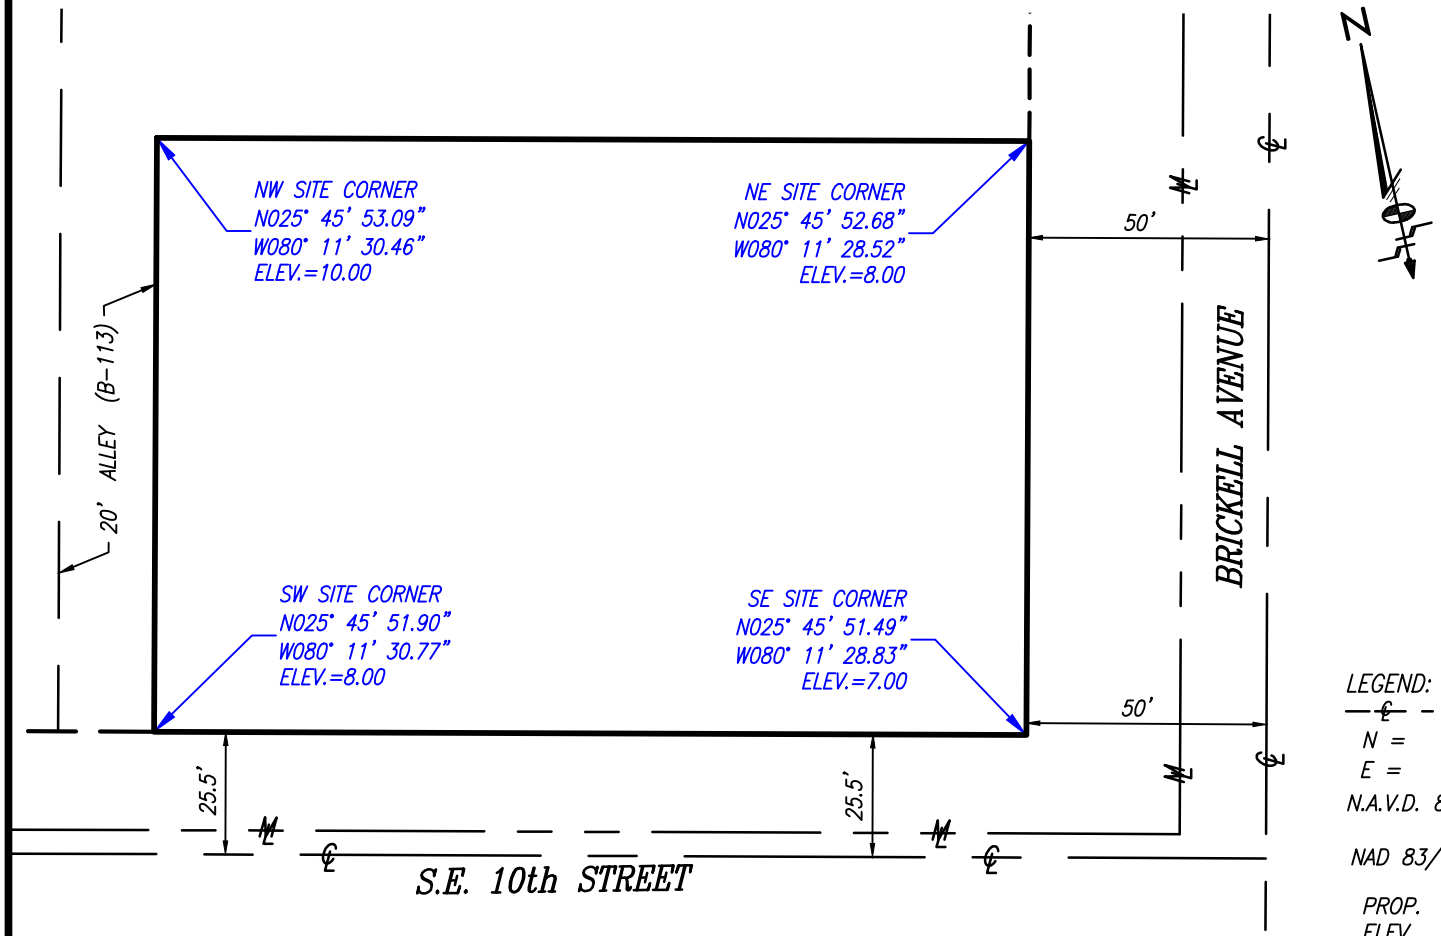

I CERTIFY THAT THESE COORDINATES ARE ACCURATE TO WITHIN ±20 FEET HORIZONTALLY; AND THE ELEVATION IS ACCURATE TO WITHIN ± 3 FEET VERTICALLY. THE HORIZONTAL DATUM (COORDINATES) FOR THE SITE ARE IN TERMS OF THE NORTH AMERICAN DATUM OF 1983 (NAD 83/90) AND ARE EXPRESSED AS DEGREES, MINUTES AND SECONDS, TO THE NEAREST HUNDREDTH OF A SECOND. THE VERTICAL DATUM (HEIGHTS) ARE IN TERMS OF THE NORTH AMERICAN VERTICAL DATUM OF 1988 AND ARE DETERMINED TO THE NEAREST FOOT. ELEVATIONS FOR SITE ARE GROUND LEVEL.

LEGEND:

— ℄ —	DENOTES CENTER LINE
N =	DENOTES LATITUDE Degrees Minutes Seconds (DMS)
E =	DENOTES LONGITUDE Degrees Minutes Seconds (DMS)
N.A.V.D. 88	DENOTES NORTH AMERICAN VERTICAL DATUM OF 1988
NAD 83/90	DENOTES NORTH AMERICAN DATUM 1983 1990 ADJUSTMENT
PROP.	DENOTES PROPOSED
ELEV.	DENOTES ELEVATION
R/W	DENOTES RIGHT OF WAY LINE
PL	DENOTES PROPERTY LINE

Schwebke-Shiskin & Associates, Inc.

LAND SURVEYORS–ENGINEERS–LAND PLANNERS – 3240 CORPORATE WAY–MIRAMAR, FL 33025

PHONE No.(954)435–7010 FAX No. (954)438–3288

THE SEAL APPEARING ON THIS DOCUMENT WAS AUTHORIZED BY MARK STEVEN JOHNSON, P.S.M. 4775

ORDER NO. 214483

DATE: MARCH 18, 2022

THIS IS NOT A " BOUNDARY SURVEY"

CERTIFICATE OF AUTHORIZATION No. LB–87

PREPARED UNDER MY SUPERVISION:

Mark Steven Johnson

MARK STEVEN JOHNSON, PRINCIPAL

FLORIDA PROFESSIONAL LAND SURVEYOR No. 4775

MARK STEVEN JOHNSON LICENSE STATE OF FLORIDA PROFESSIONAL SURVEYOR AND MAPPER

REVISIONS

NO. DATE

Mark S Johnson

Digitally signed by Mark S Johnson
DN: CN=Mark S Johnson, O=Schwebke-Shiskin and Associates, C=US
Location: Miramar, FL
Reason: THE SEAL ON THIS DOCUMENT WAS AUTHORIZED BY MARK STEVEN JOHNSON, PSM 4775 ON THE DATE BELOW
Contact Info: 954-435-7010
Date: 2022.03.30 13:49:47-04'00'

GRAPHIC SCALE

40' 0 20' 40'

1 INCH = 40 FEET

K:\395441\MARY BRICKELLS ADDN BLK 101S\FAA\DWG\BLOCK 101S FAA.DWG